


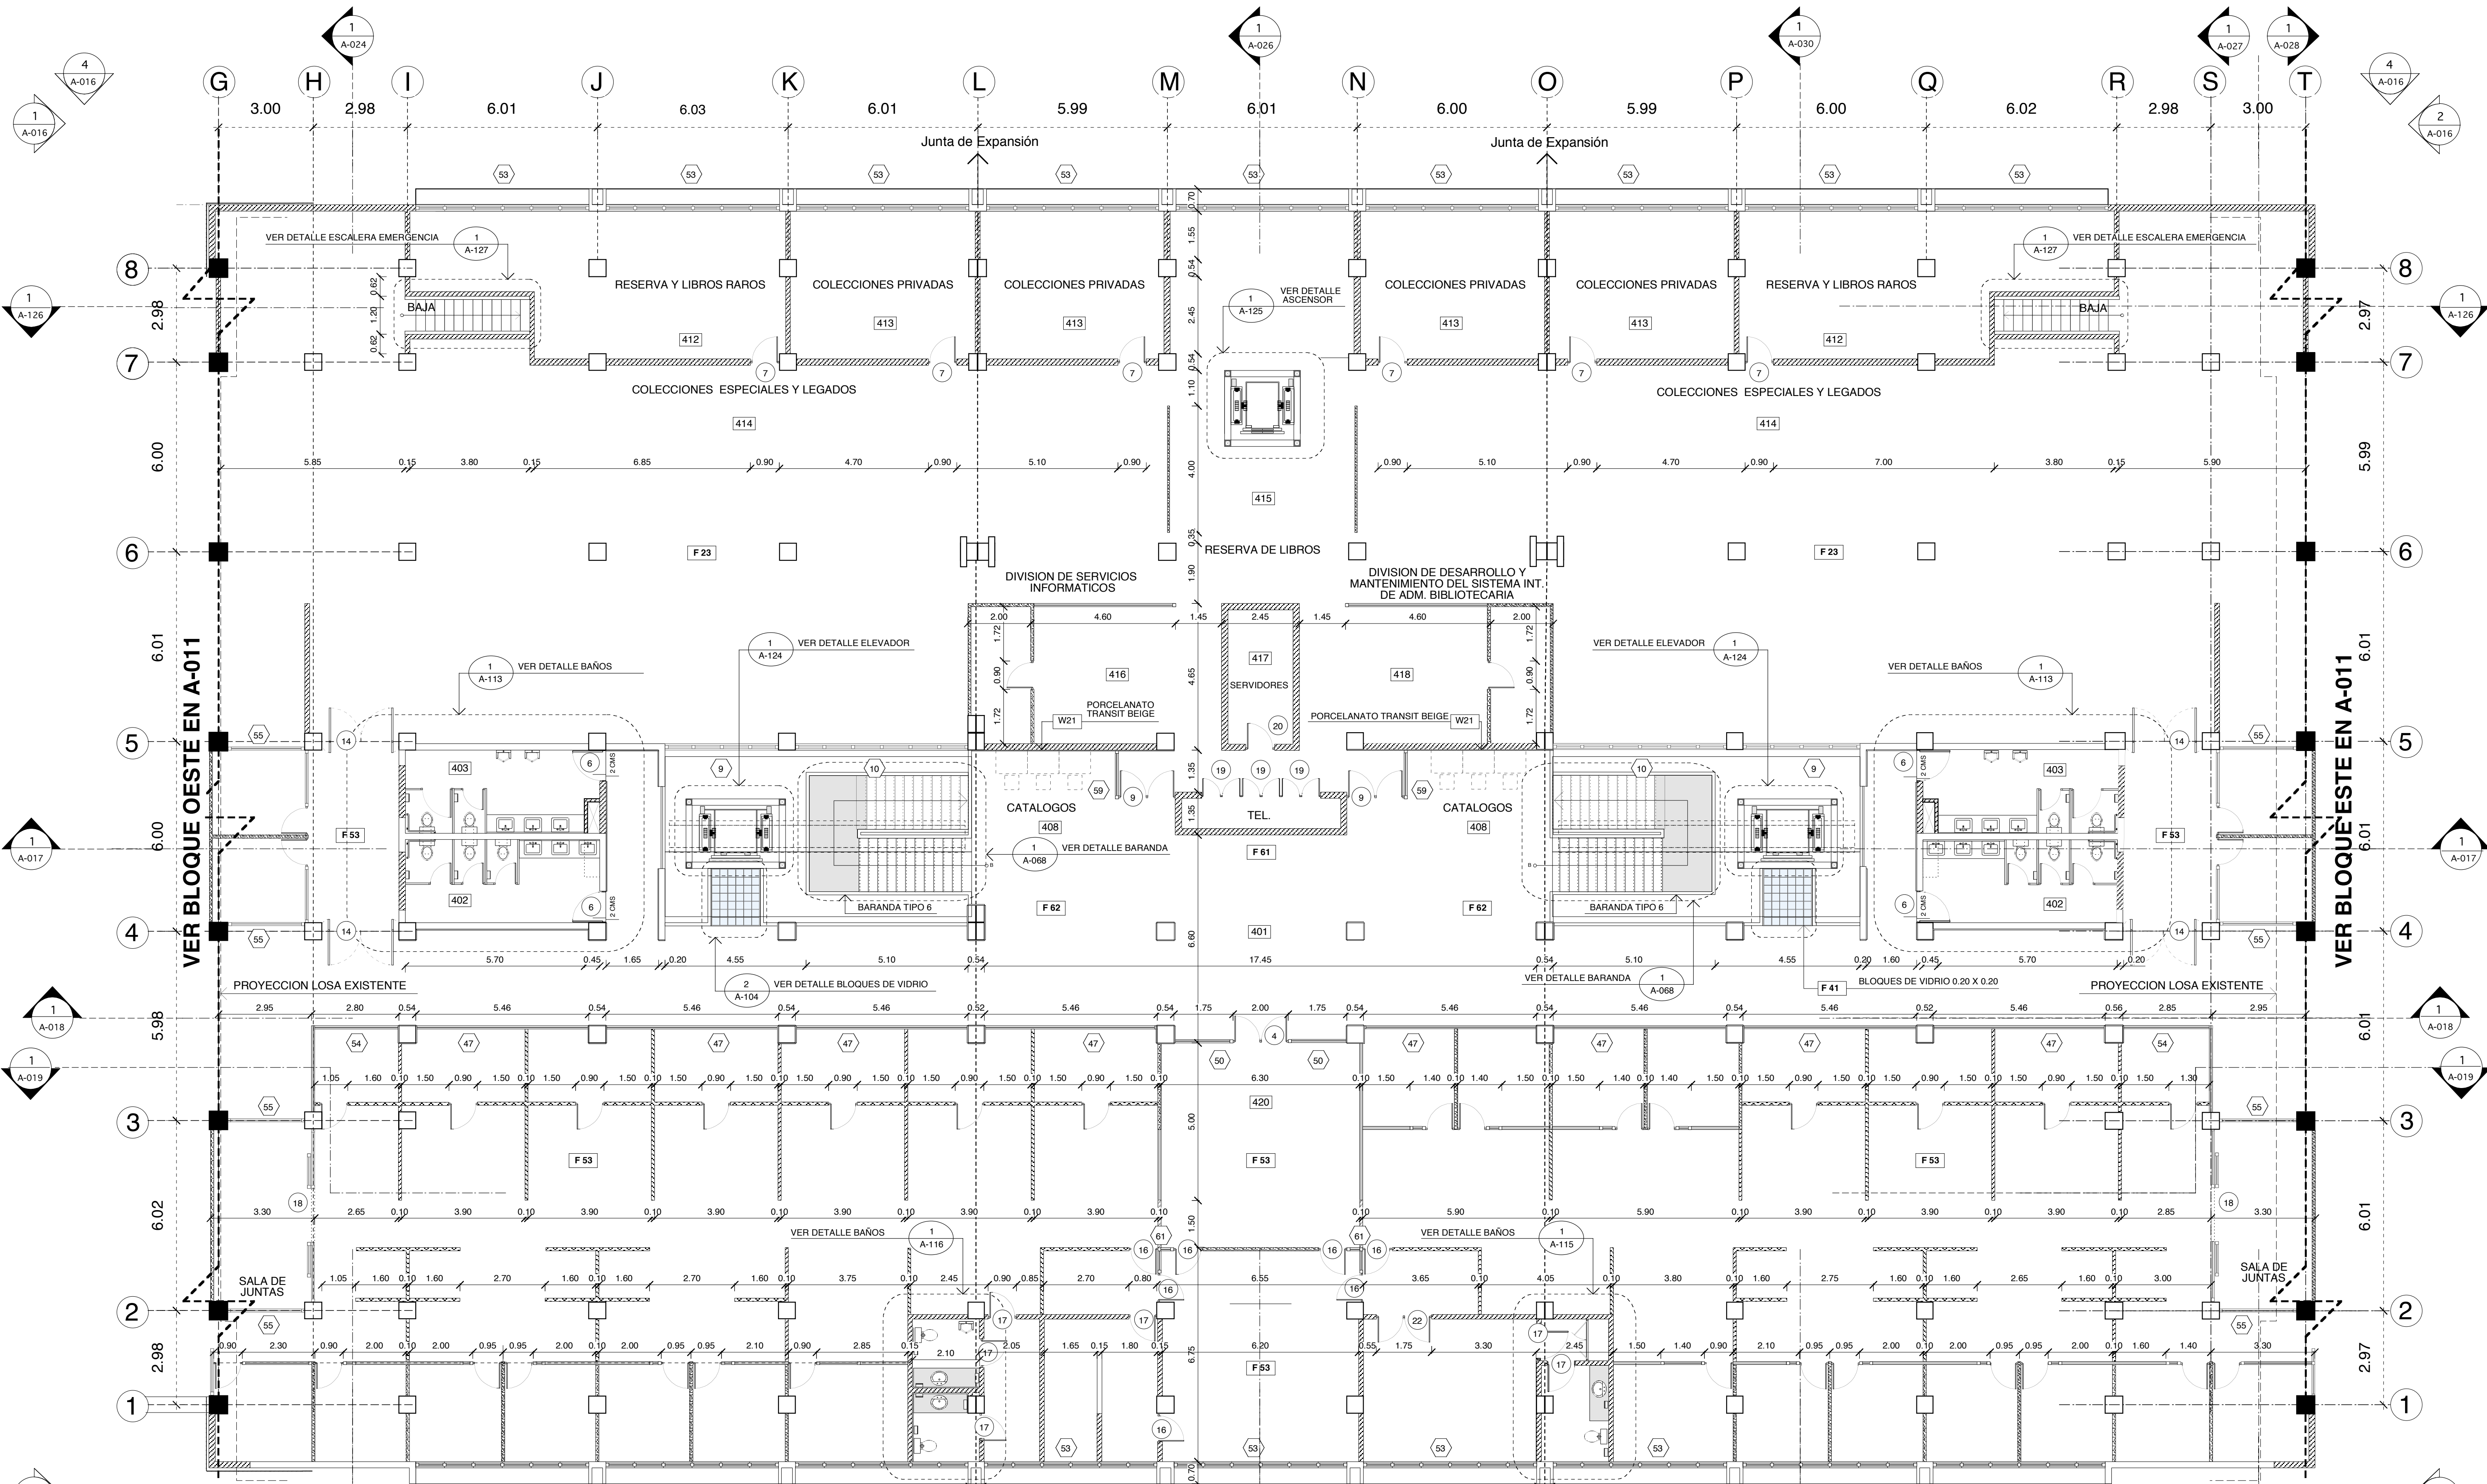

LEYENDA

- 401 LOBBY
- 402 BAÑOS HOMBRES
- 403 BAÑOS MUJERES
- 404 KITCHENNETTE
- 405 COPIADORA/FAX
- 406 ESCALERA
- 407 ESCALERA DE EMERGENCIA
- 408 CATALOGOS
- 409 CUARTO AIRE ACONDICIONADO
- 410 MANTENIMIENTO
- 411 ALMACEN
- 412 RESERVA Y LIBROS RAROS
- 413 COLECCIONES PRIVADAS
- 414 RESERVA DE LIBROS
- 415 COLECCIONES ESPECIALES Y LEGADOS
- 416 DIV. DE SERVICIOS INFORMATICOS
- 417 SERVIDORES
- 418 DIV. DE DES. Y MANT. DEL SIST. INT. DE ADM. BIBLIOTECARIA
- 419 SALA DE REVISTAS
- 420 OFICINAS
- 421 SALA DE PERIODICOS
- 422 AREA DE LECTURA

LEYENDA DE MATERIALES

- MUROS DE BLOQUES EXISTENTES
- MUROS DE BLOQUES PROPUESTOS
- SISTEMA A 62" (1.57 MT.)
- SISTEMA A 86" (2.18 MT.) DE ALTURA CON DINTEL EN SHEET-ROCK DE 2.18 A 3.00
- DIVISION EN YESO A 3.00 MT. DE ALTURA
- SISTEMA A 1.00 MT. DE ALTURA

VER PLANTA AMUEBLADA A-042
VER PLANTA PISOS A-053
VER PLANTA PLAFONES A-064

PLANTA ARQUITECTÓNICA BLOQUE CENTRAL
CUARTO NIVEL

1 A-012

ESCALA 1:100

0 1 2 5 10 15 Mts.



PROPIETARIO:
Oficina de Ingenieros Supervisores de Obras del Estado

PROYECTO:
Ampliación y Remodelación Biblioteca Nacional P.H.U.



SECRETARÍA DE ESTADO DE CULTURA



PROYECTO:
Ampliación y Remodelación Biblioteca Nacional P.H.U.



Caralva S.A. & Moré Arquitectos

PROYECTO:
Ampliación y Remodelación Biblioteca Nacional P.H.U.

PROYECTO:
Ampliación y Remodelación Biblioteca Nacional P.H.U.

